


TUBE LENGTH 6103

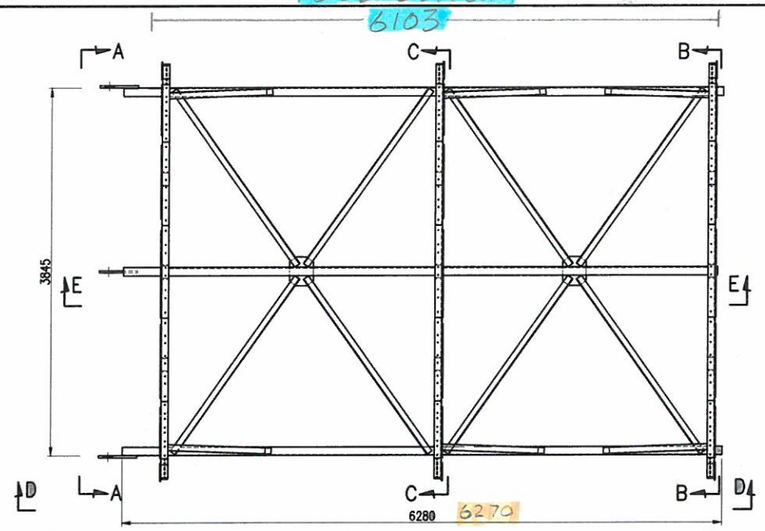

LIFTING FRAME PLAN

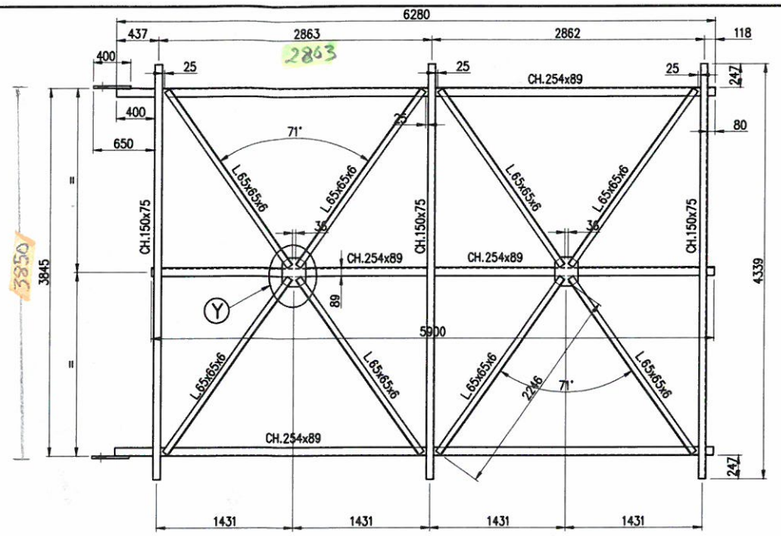


SECTION "F-F"
BOTTOM STEEL FRAME

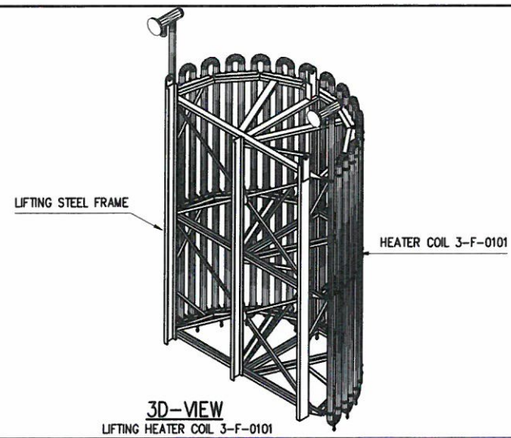


3D-VIEW
LIFTING HEATER COIL 3-F-0101

BILL OF MATERIALS


ITEM	SIZE	DESCRIPTION	QTY	MATERIAL No.
1	254x89x36 CHANNEL MILD STEEL GR 43A TO BS 4360		20.00M	***
2	150x75x10x5.5 CHANNEL MILD STEEL GR 43A TO BS 4360		60.00M	***
3	65x65x8 EQUAL ANGLE MILD STEEL GR 43A TO BS 4360		40.0M	***
4	20mm THICK PLATE MILD STEEL GR 43A TO BS 4360		0.40M^2	***
5	10mm THICK PLATE MILD STEEL GR 43A TO BS 4360		2.80M^2	***
6	ø8 STUD BOLTS & NUT TO BS 4190		168.0 PCS.	***
	NOTE: BILL OF MATERIALS ARE FOR ONE UNIT ONLY			

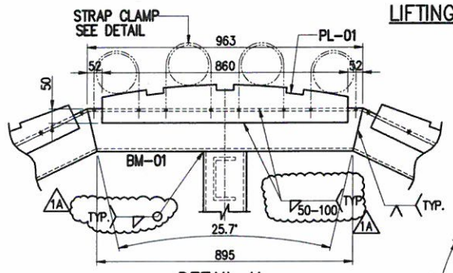


DETAIL-X
LIFTING PL. OMITTED

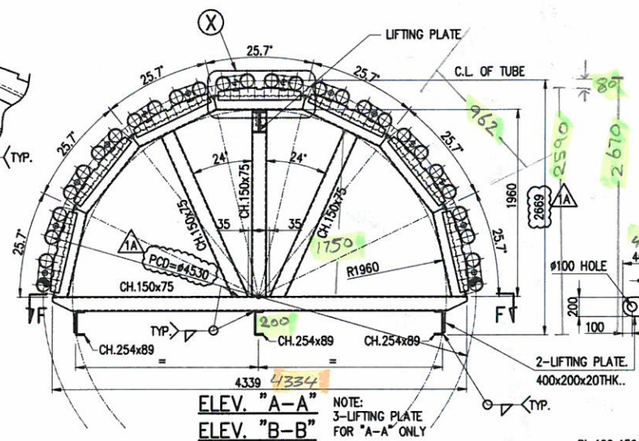


ELEV. "A-A"
ELEV. "B-B"
NOTE:
3-LIFTING PLATE FOR "A-A" ONLY

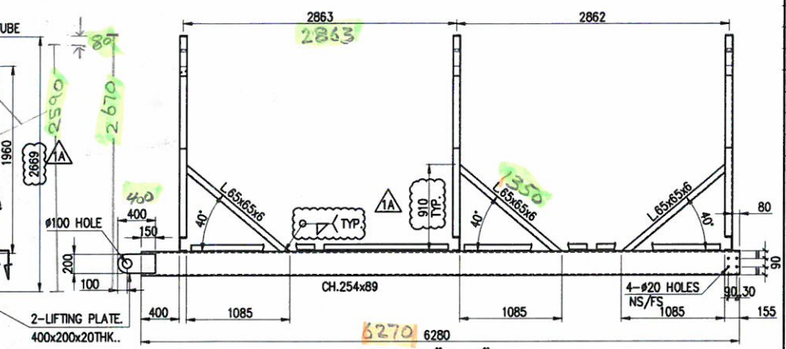


ELEV. "D-D"

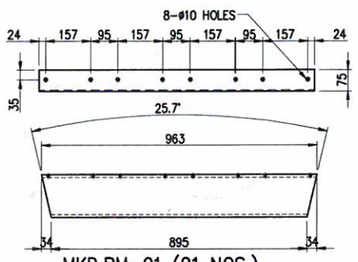


MKD.BM-01 (21 NOS.)
CH. 150x75x10x5.5

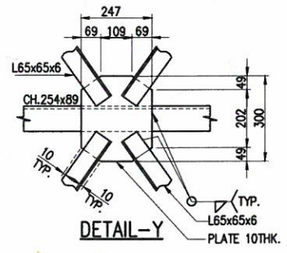


DETAIL-Y

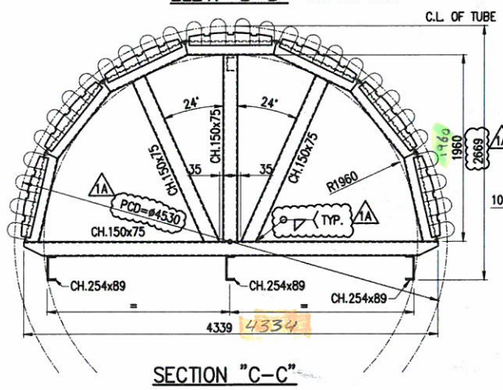


SECTION "C-C"

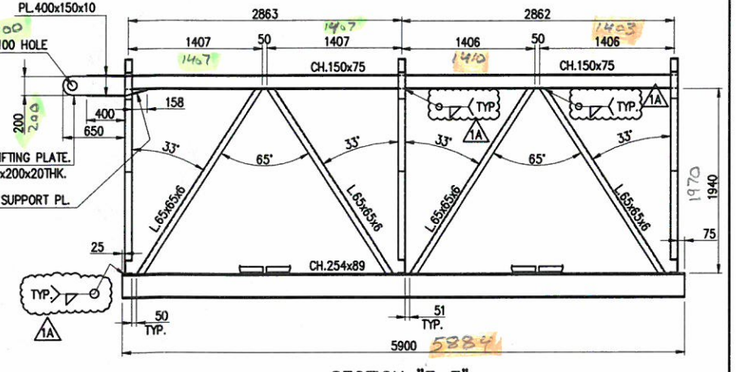

SECTION "E-E"

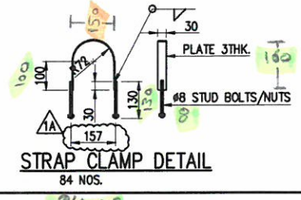

STRAP CLAMP DETAIL
84 NOS.

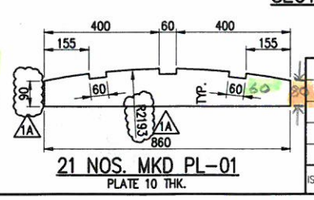

21 NOS. MKD PL-01
PLATE 10 THK.

GENERAL NOTES:

1) ALL PERMANENT STEELWORKS SHALL BE PAINTED WITH ADGAS SOP. 022.
2) ALL WELDS SHALL BE IN ACCORDANCE WITH ADGAS WELDING PROCEDURE SOP. 042.
3) ALL STEEL SHALL BE GRADE S275 JR TO BS EN 10025.
4) ALL STEEL FABRICATION OF STEELWORKS SHALL COMPLY WITH AISC OR BS EN 10025.
5) ALL WELDS SHALL BE 6mm FILLET AND CHECKED WITH MAGNETIC PARTICLE INSPECTION.
6) STRUCTURAL STEELWORKS SHALL BE IN ACCORDANCE WITH ADGAS SPECIFICATION FOR STEEL FABRICATION AND ERECTION.
7) ALL DIMENSIONS ARE IN MILLIMETERS UNLESS NOTED OTHERWISE.

Dimension verification Date: 8-JAN-2015

RE-ISSUED FOR CONSTRUCTION

REFERENCE DRAWING:

DETAILS OF HEATER COIL,,,,	AC-3-A1F-2-14803

ISSUE	DATE	REMARKS	DRN	CHK	ENG
1A	07.01.2015	RE-ISSUED FOR CONSTRUCTION	GBA	EYL AKR	DNE
1	30.08.2014	ISSUED FOR CONSTRUCTION	GBA	EYL AKR	DWB


DO NOT SCALE THIS PRINT
ALL DIMENSIONS ARE IN mm UNLESS OTHERWISE NOTED
SCALE: AS NOTED

ABU DHABI GAS LIQUEFACTION COMPANY LIMITED


MOD No. SD/1/009/13	TITLE	LIFTING FRAME FOR INSTALLATION OF HEATER COIL FOR 3-F-0101 PLAN ELEVATION AND DETAILS	
TRAIN 1	DRG No.	A-3-A1M-1-15253	ISSUE 1A

THIS BORDER IS FOR ADGAS INTERNAL USE ONLY. CAD FILE No.: A3A1M115253


84 NOS.

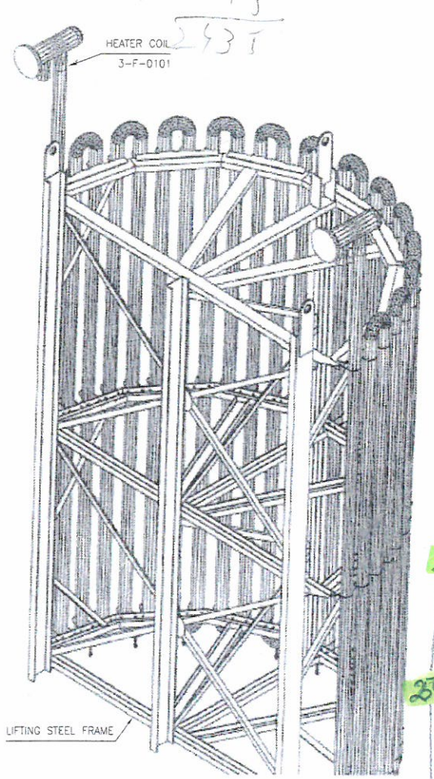


3D- VIEW

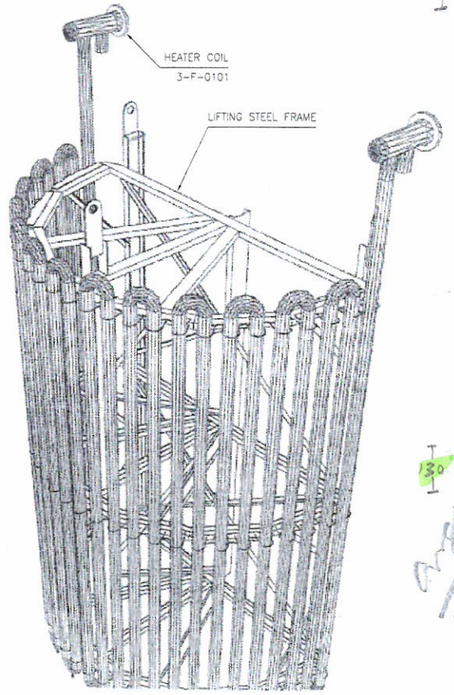


3D- VIEW

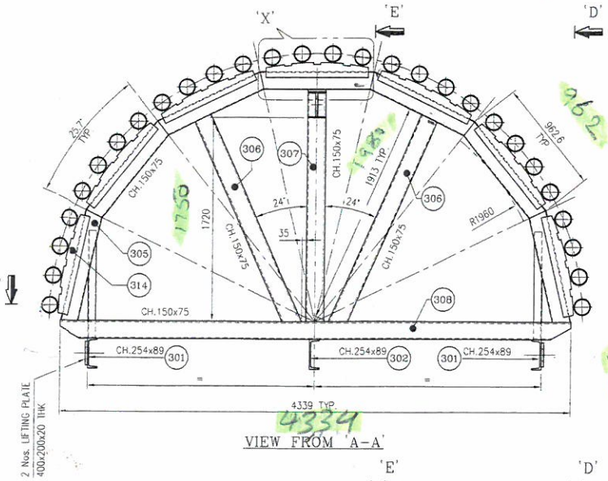


VIEW FROM 'A-A'

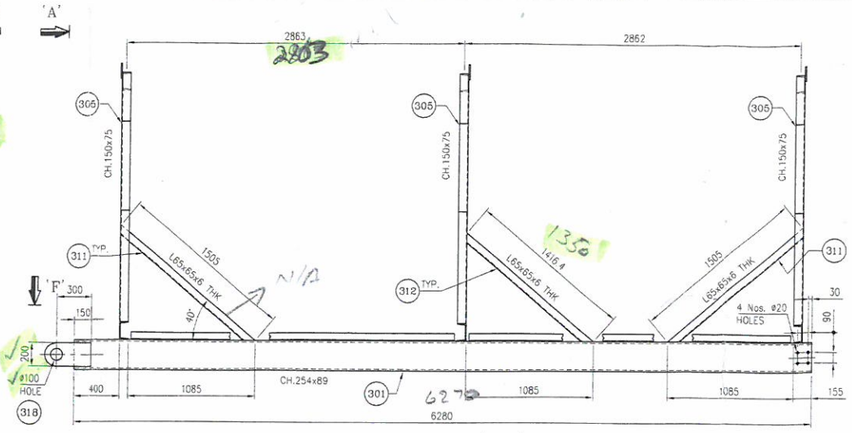


ELEVATION AT 'D-D'

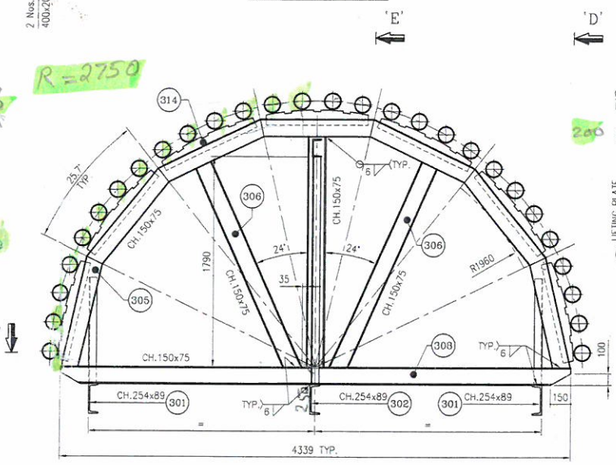


VIEW FROM 'C-C'

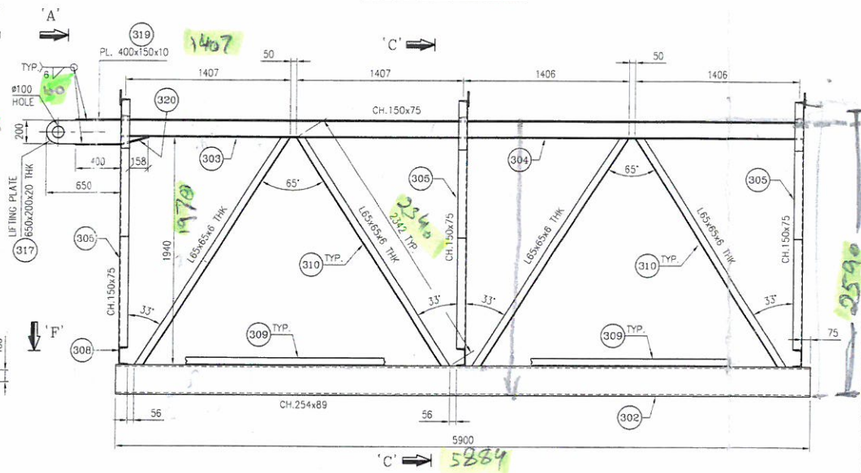


ELEVATION AT 'E-E'

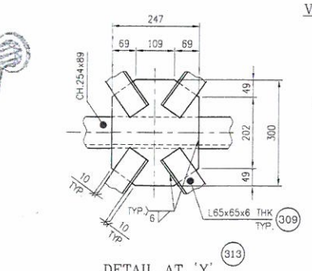


DETAIL AT 'Y'

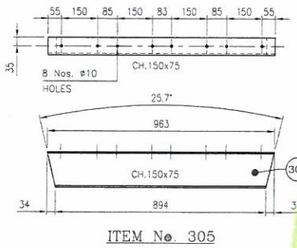


ITEM No. 305

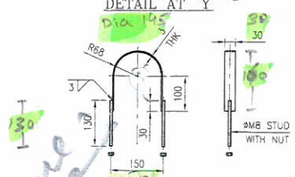


STRAP CLAMP

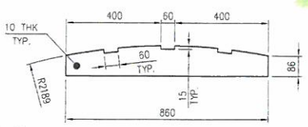

ITEM No. 314

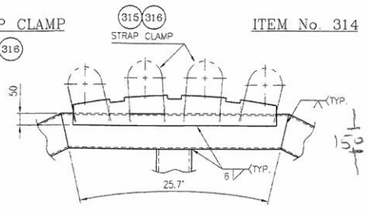

DETAIL AT 'X'

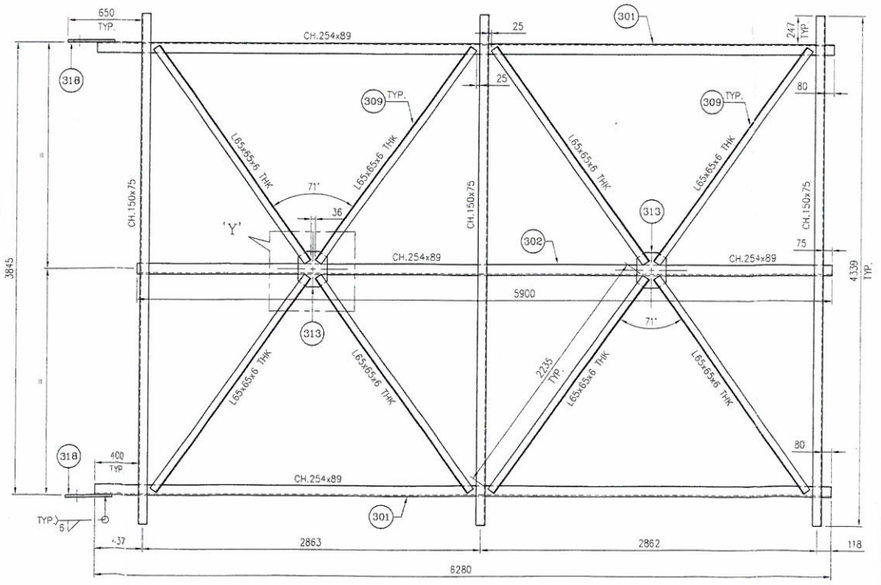

SECTION AT 'F-F'
(BOTTOM STEEL FRAME)

NOTES

1. ALL DIMENSIONS ARE IN mm. UNLESS OTHERWISE SPECIFIED.
2. ALL STEELWORKS SHALL BE PAINTED WITH ADGAS SOP. 022
3. ALL STEEL FABRICATION OF STEEL WORKS SHALL COMPLY WITH AISC OR BS EN 10025
4. ALL WELDS SHALL BE 6mm AND CHECKED WITH MAGNETIC PARTICLE INSPECTION.

CLIENT TO PROVIDE PAINTING SPECIFICATION
ADGAS SOP. 022

REFERENCE DRAWINGS

SR.No.	TITLE	DRAWING No.
1	LIFTING FRAME FOR INSTALLATION OF HEATER COIL FOR 3-F-0101	A-3-A1M-1-15253 (R1)
2	LIFTING FRAME FOR INSTALLATION OF HEATER COIL FOR 3-F-0201	A-3-A1M-2-13950 (R2)

ITEM No.	QTY.	DESCRIPTION	DIMENSION/SIZE	MATERIAL	WT. Kg.	REMARKS
320	1	SUPPORT PLATE	10 THK x 234 x 150	A-36	3	
319	2	LIFTING LUG SUPPORT PLATE	10 THK x 400 x 150	A-36	9.5	
318	2	LIFTING LUG	20 THK x 400 x 200	A-36	25	
317	1	LIFTING LUG	20 THK x 650 x 200	A-36	20	
316	168	HEX. HD. NUT	#M8	A-194 Gr. 2H	-	
315	84	'U' SUPPORT CLAMP	#M8 (REFER DETAIL)	A-36	10	
314	21	GUIDE PLATE FOR COILS	10 THK x 860 x 128	A-36	181.5	
313	2	SUPPORT PLATE	10 THK x 300 x 247	A-36	11.8	
312	2	ANGLE	L65 x 53 x 6 x 1416 LG.	A-36	17	
311	4	ANGLE	L65 x 65 x 6 x 1505 LG.	A-36	35.6	
310	4	ANGLE	L65 x 65 x 6 x 2342 LG.	A-36	55	
309	8	ANGLE	L65 x 65 x 6 x 2235 LG.	A-36	106	
308	3	CHANNEL	CH.150x75x10x5.5x4339 LG.	A-36	242	
307	3	CHANNEL	CH.150x75x10x5.5x1960 LG.	A-36	109	
306	6	CHANNEL	CH.150x75x10x5.5x191.3 LG.	A-36	212	
305	21	CHANNEL	CH.150x75x10x5.5x963 LG.	A-36	352	
304	1	CHANNEL	CH.150x75x10x5.5x2855 LG.	A-36	53	
303	1	CHANNEL	CH.150x75x10x5.5x2924 LG.	A-36	55	
302	1	CHANNEL (BS4 : PART 1)	CH.254 x 89 x 5900 LG.	A-36	211	
301	2	CHANNEL (BS4 : PART 1)	CH.254 x 89 x 6280 LG.	A-36	449	

BILL OF MATERIALS
(BILL OF MATERIAL FOR ONE PASS ONLY) — TOTAL WEIGHT 2160 Kgs.

Dimension verification Dated 22_DEC_2014

REV	DATE	DESCRIPTION	DRN	CHK	ENG	APP	APP. ADGAS
R0	18.11.14	ISSUED FOR APPROVAL	ASP	BR	LG	LG	-

ABU DHABI GAS LIQUEFACTION COMPANY LTD
(ADGAS)
PROJECT TITLE
DAS ISLAND

CONTRACTOR :
Serck Services (Gulf) Ltd.
Serck Heat Transfer
Industrial Area 12
P.O. BOX 5834, SHARJAH, U.A.E.
TEL : +971 6 5086600, FAX : +971 6 5584607
E-mail:- info@serckgulf.com, www.serckgulf.com.

CONTRACTOR DRAWING NUMBER: SHT-PRJ008884-001 (SHT 3 OF 3)

DRAWING TITLE
LIFTING FRAME FOR INSTALLATION OF HEATER COIL FOR 3-F-0101

CONTRACT No.	ADGAS DRAWING NUMBER	REV.
4500059689-B6	AC-3-A1M-1-0001	0

SCALE: 1 : 25 — CAD FILE No. AC3A1M10001

SD/2/007/10